

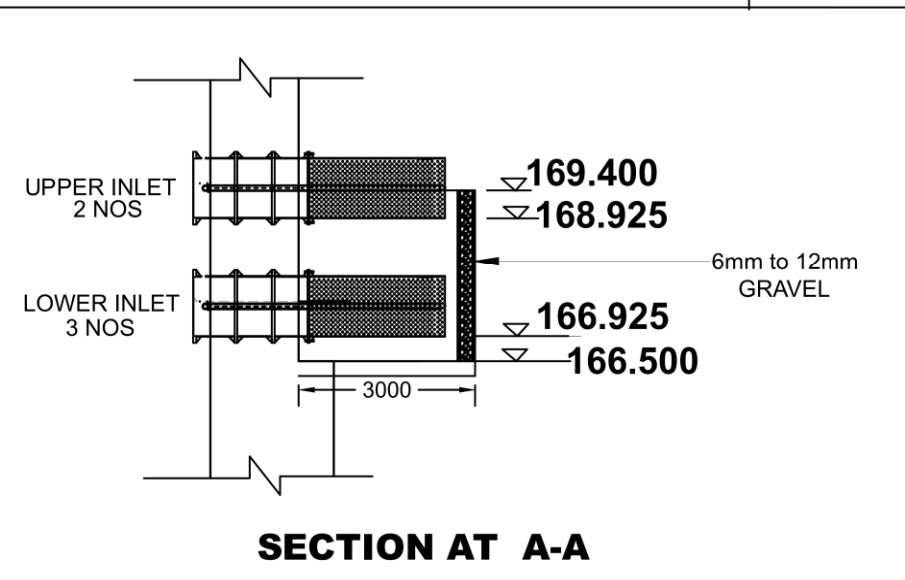
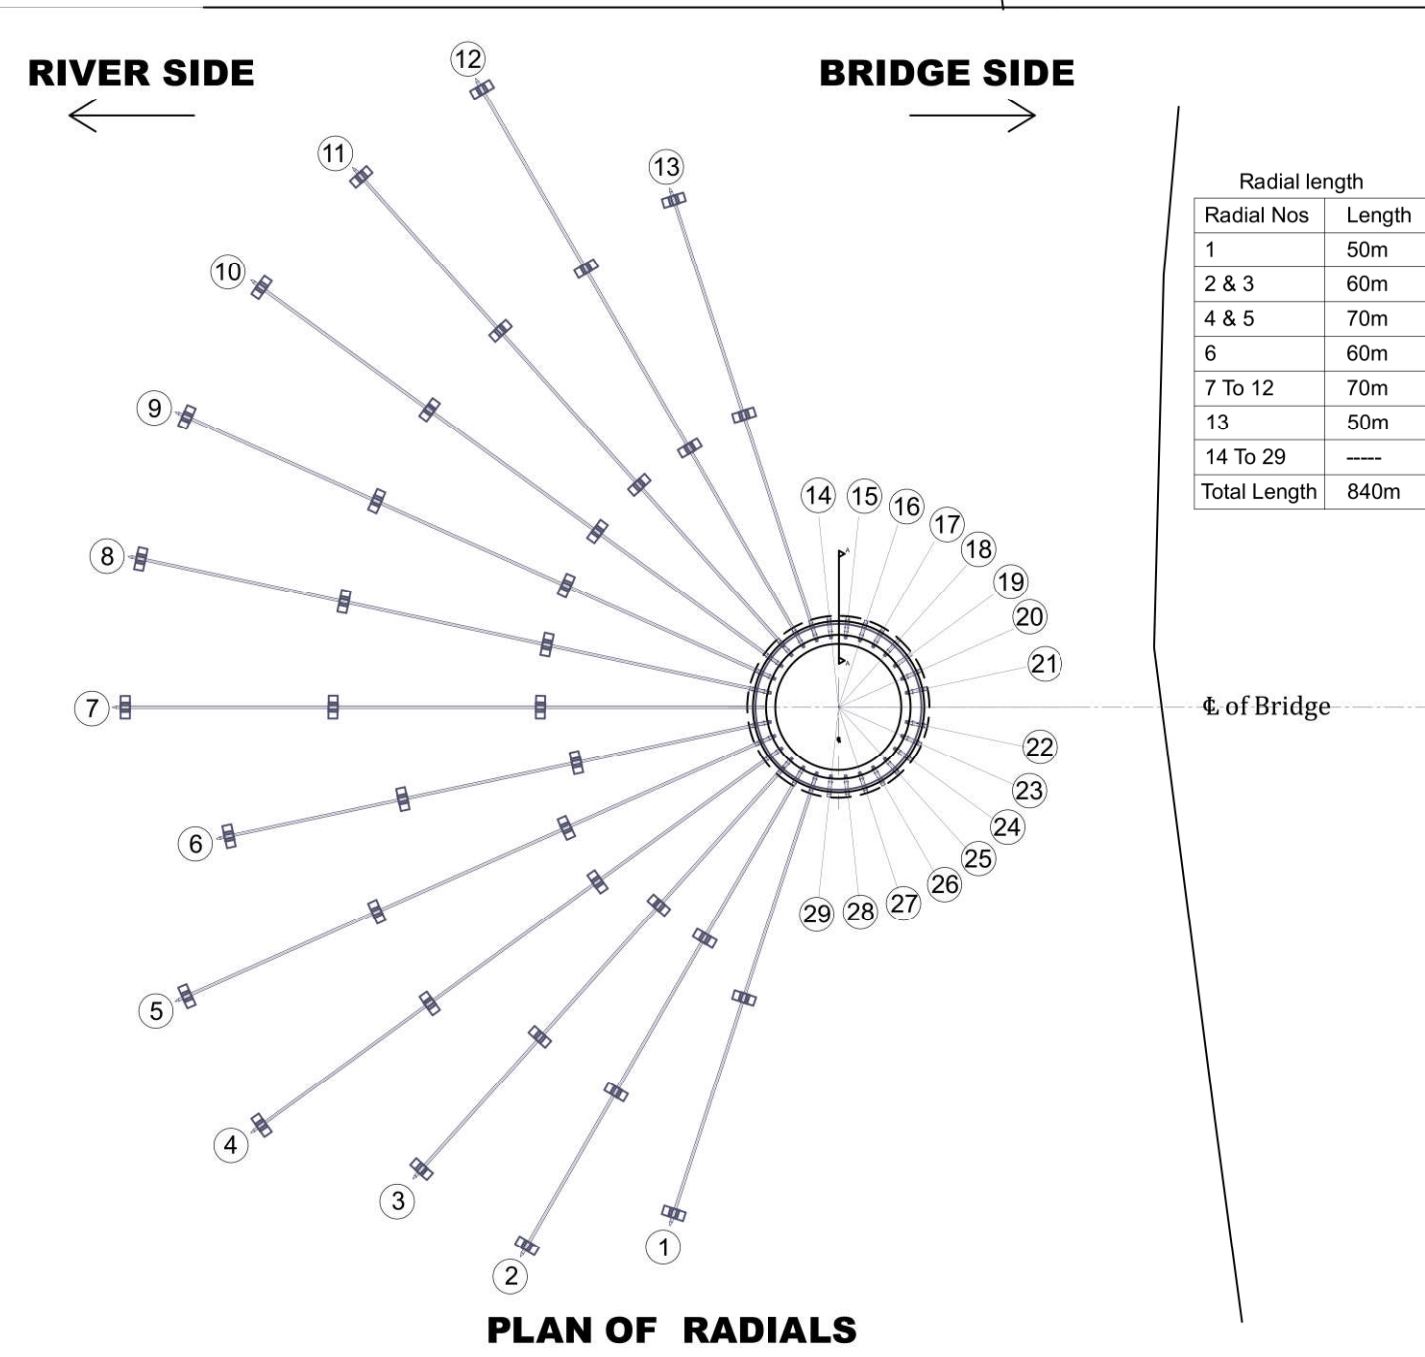
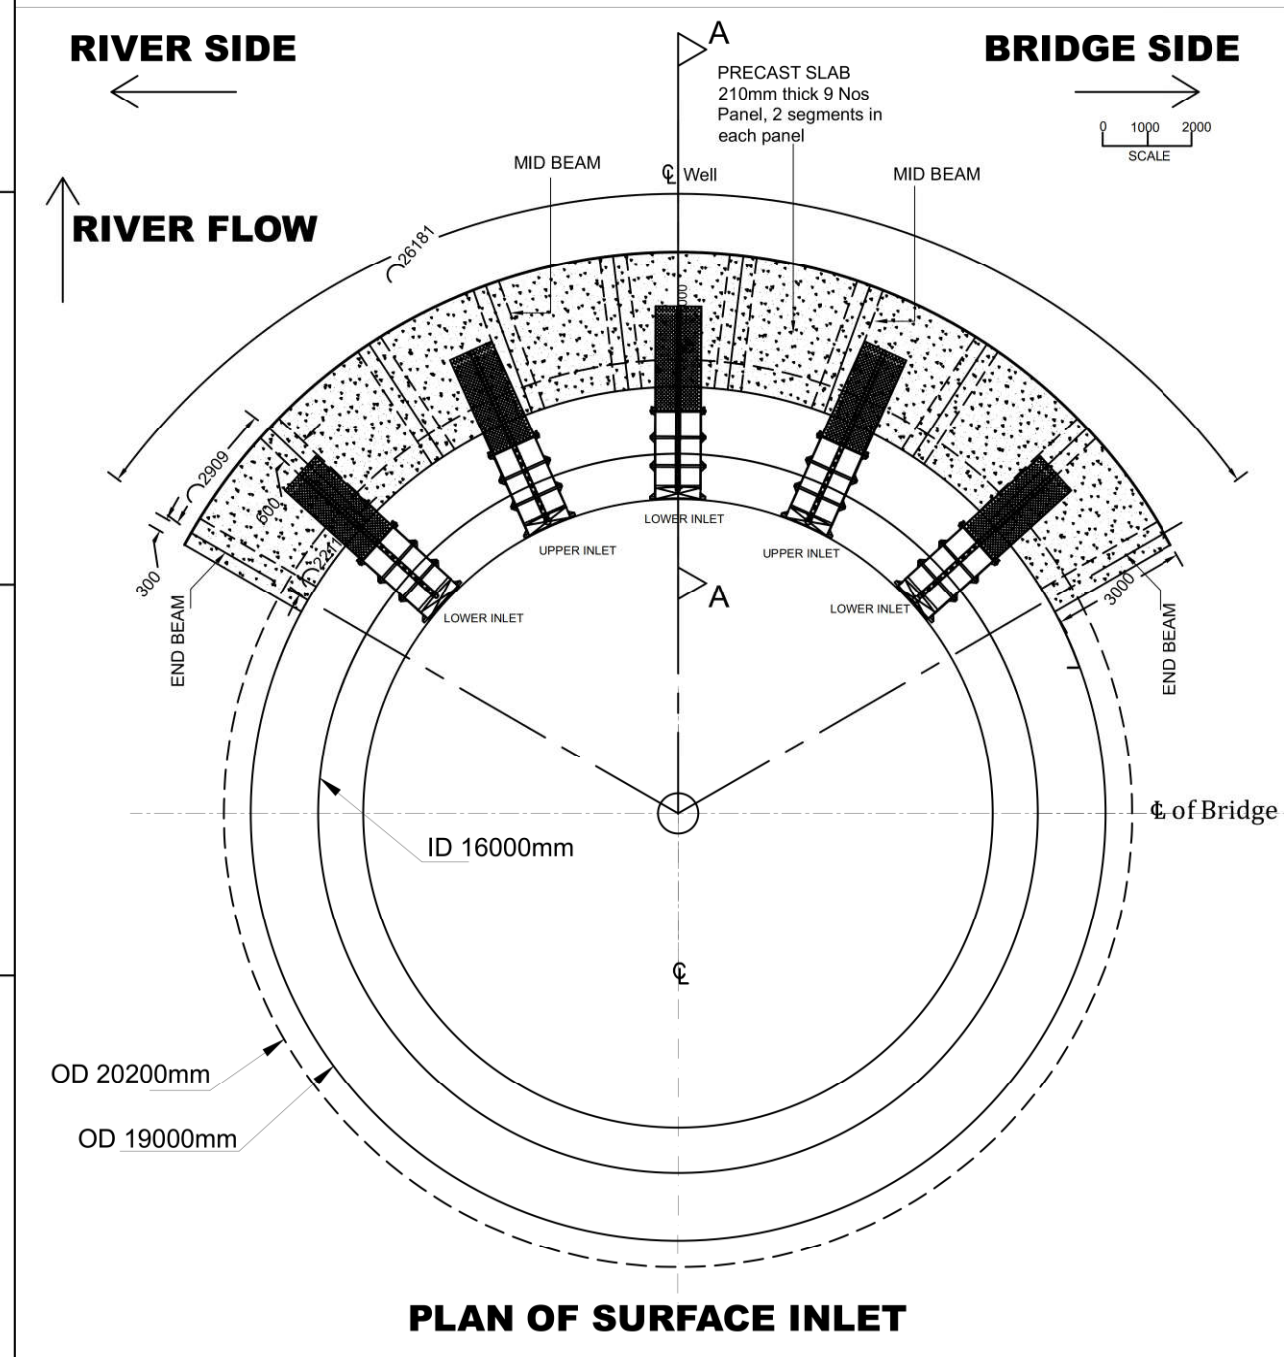
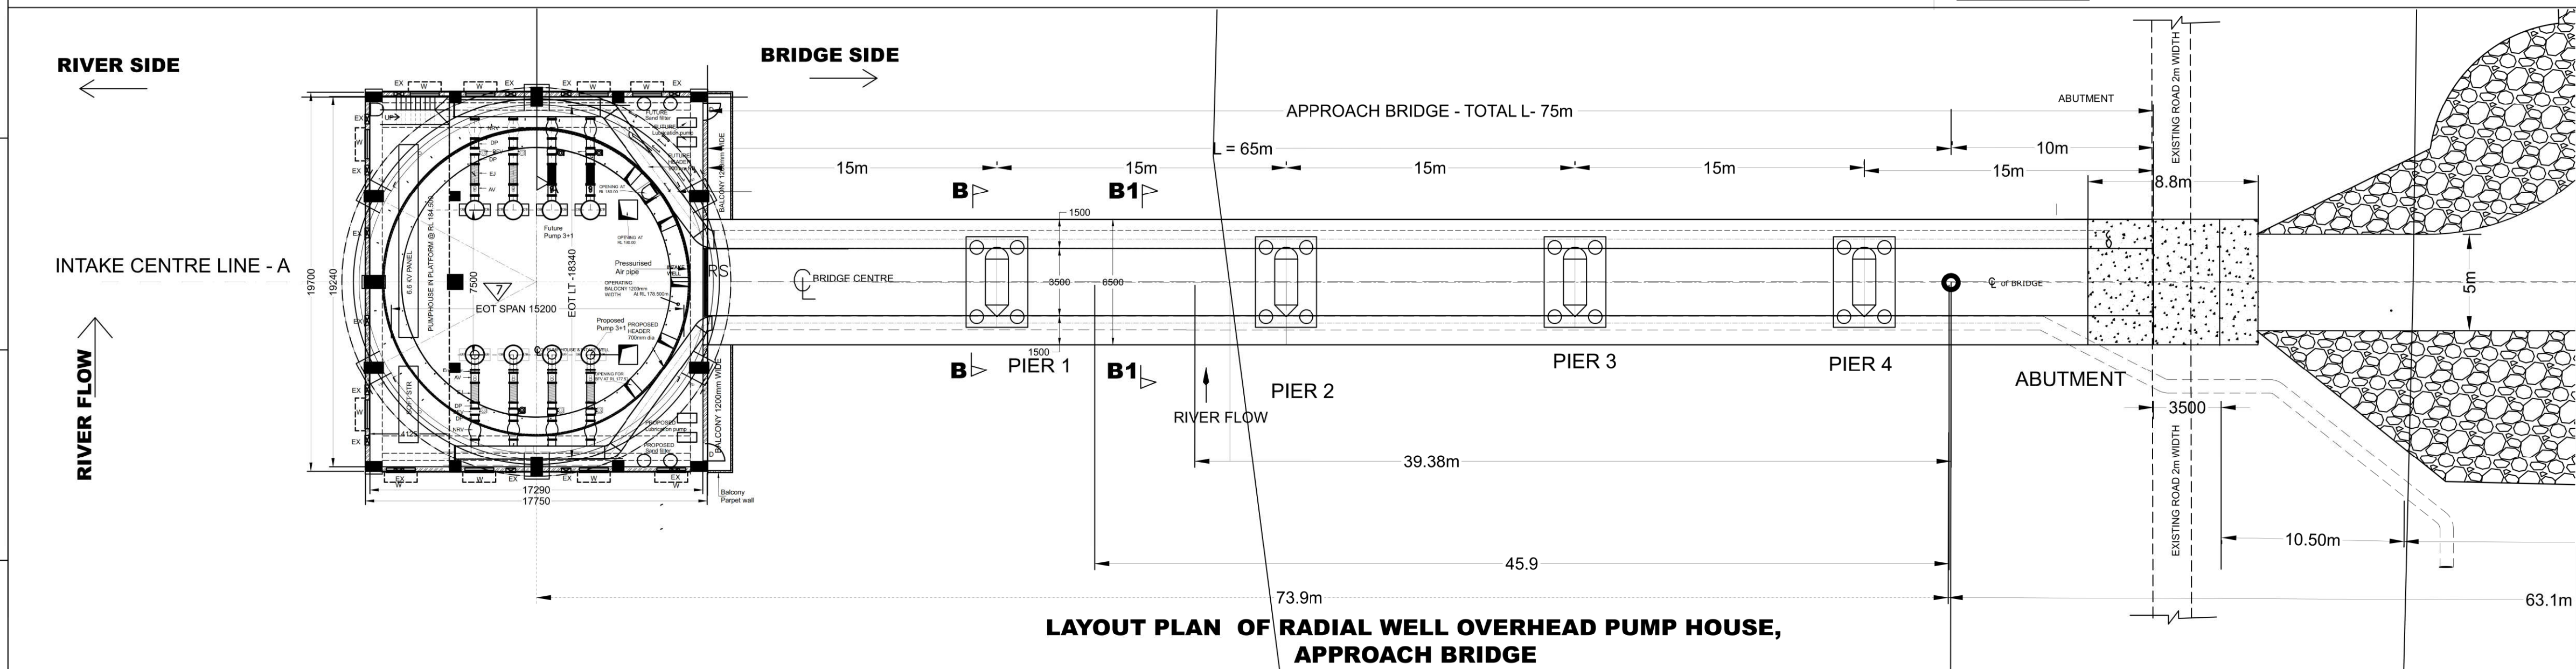
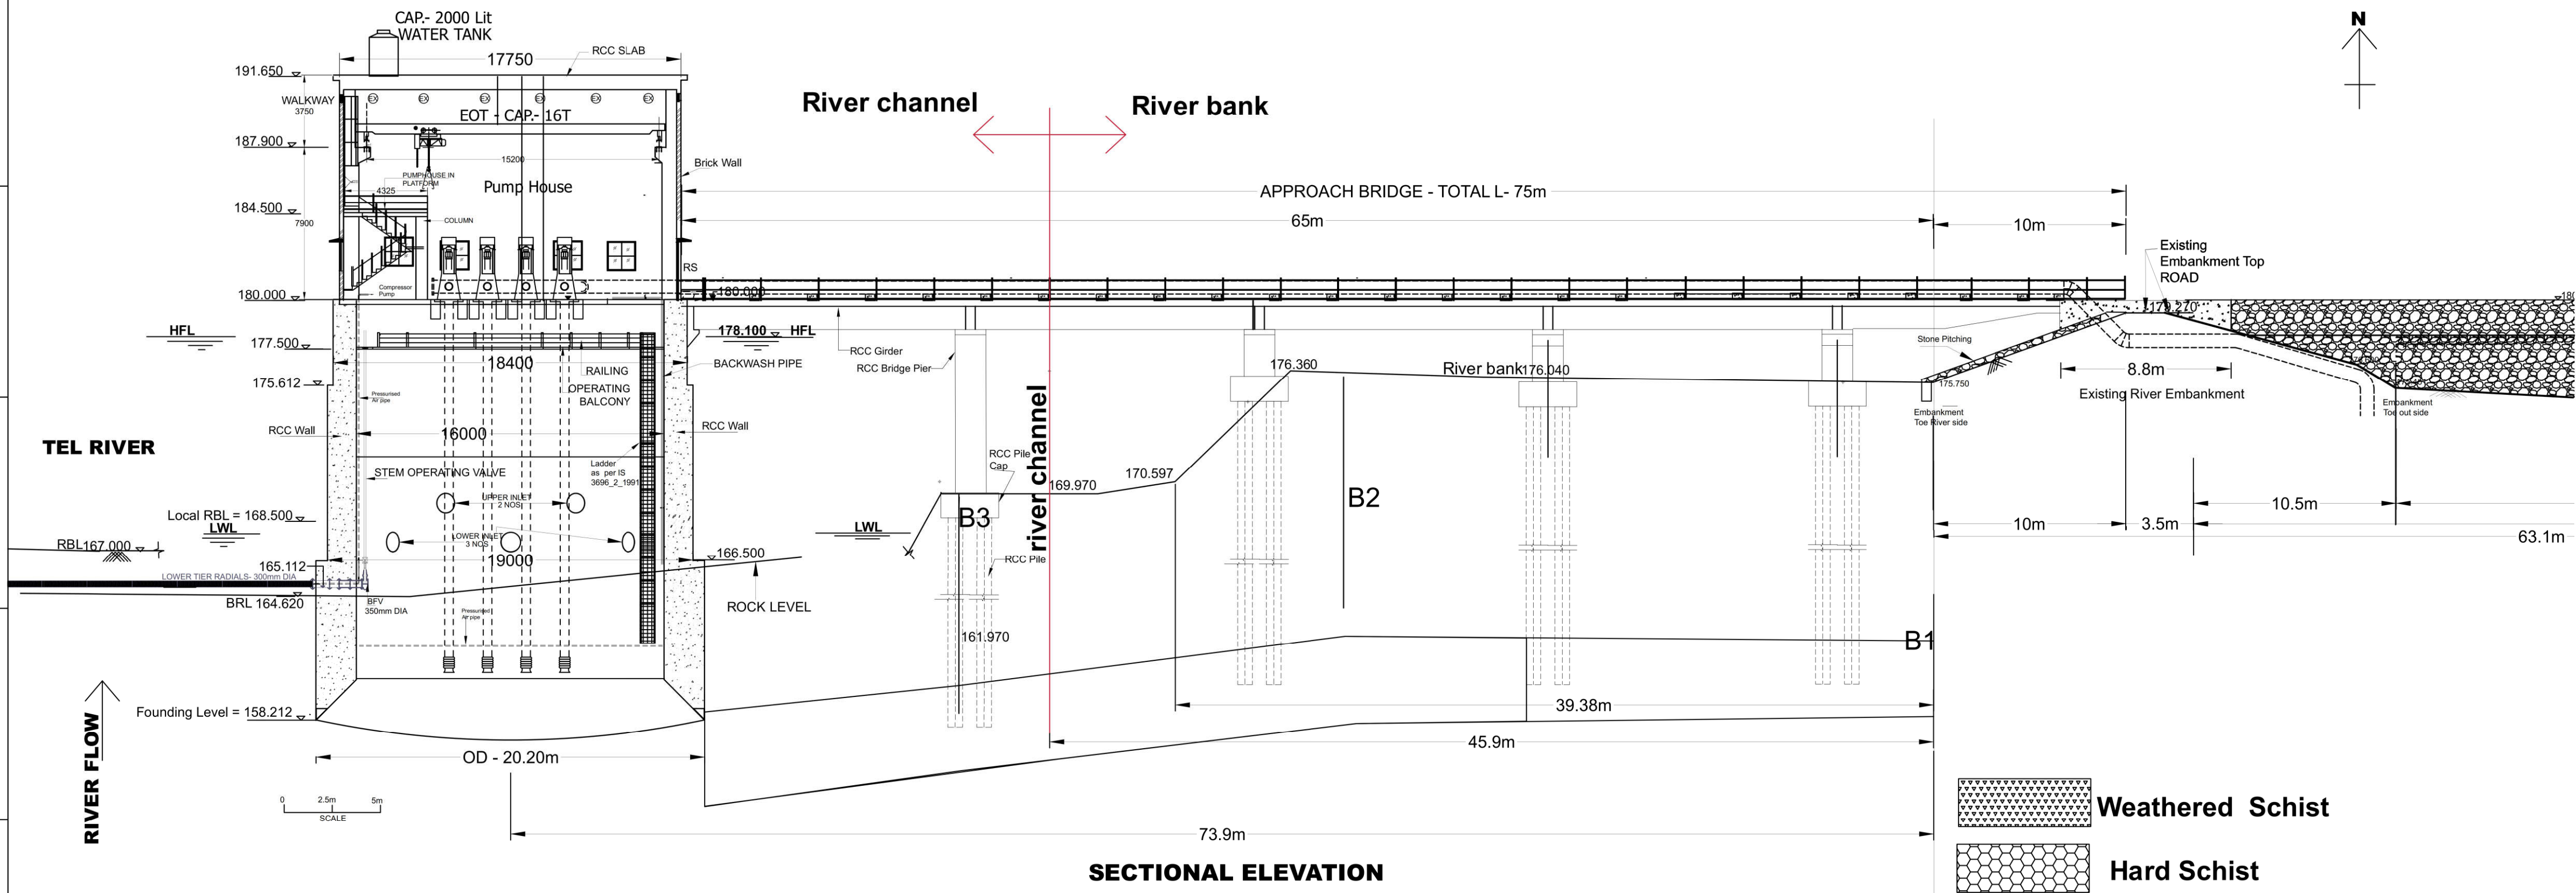


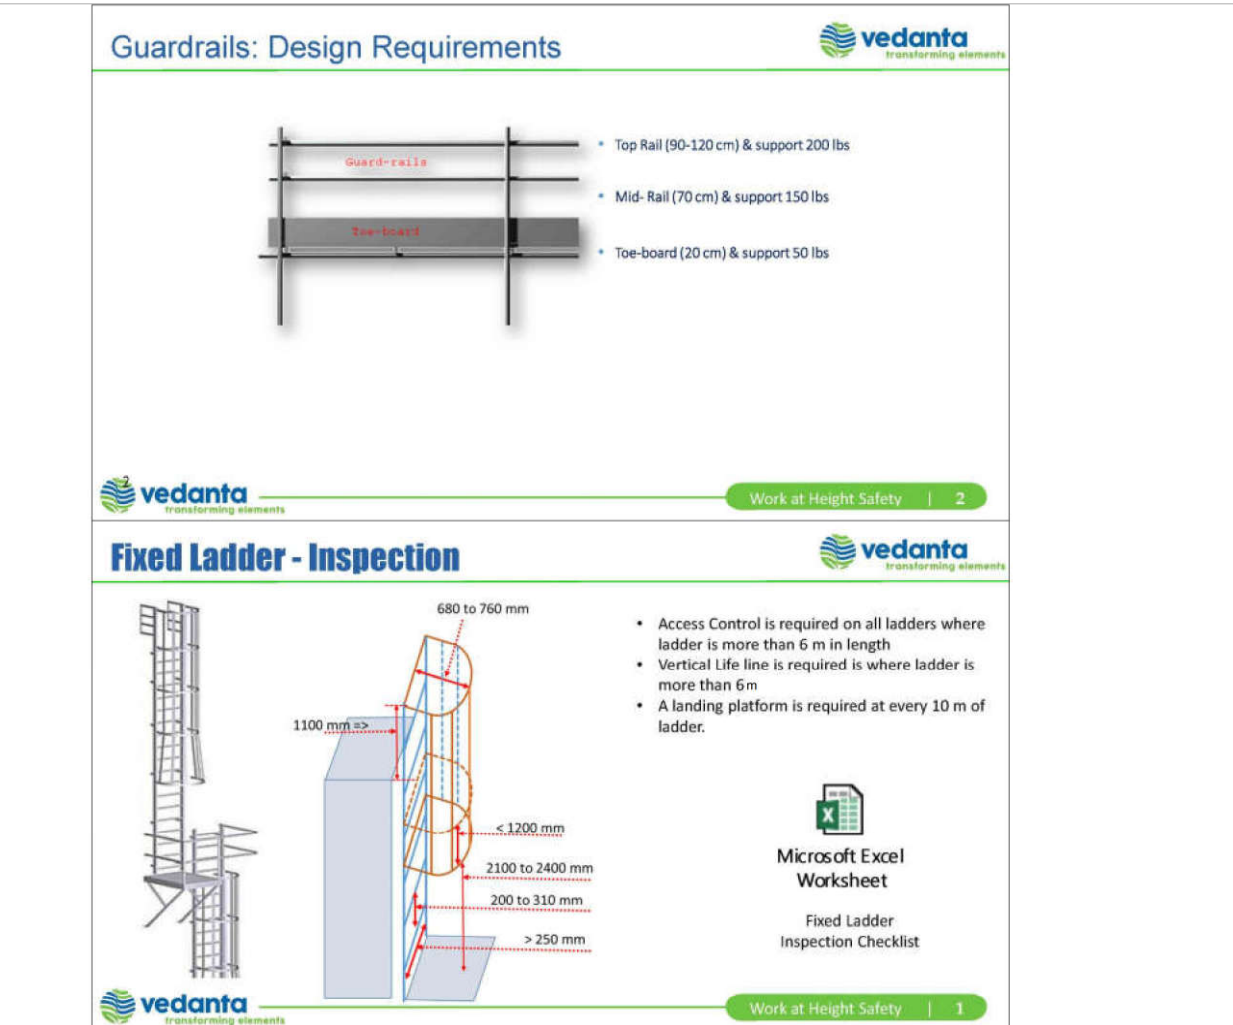

- REFERENCE DRAWING [REFER LATEST REVISION]**
- FOR DETAILS OF CUTTING EDGE FOR INTAKE WELL BY SINKING METHOD.1255-PRA-VAL-IW-C-001.
 - DETAILS OF RCC WELL STAINING AND BOTTOM PLUG. 1286-PRA-VAL-IW-C-002A
 - STRUCTURAL DETAILS OF PUMP HOUSE 1286-PRA-VAL-IW-C-003A
 - STRUCTURAL DETAILS OF PUMP HOUSE SUPERSTRUCTURE & ROOF 1286-PRA-VAL-IW-C-004A
 - ARCHITECTURAL PUMP HOUSE - 1286-PRA-VAL-IW-C-007A
 - DETAILS OF RADIALS INCLUDING END ENCOURAGE 1255-PRA-VAL-IW-C-006
 - DETAILS OF RADIAL ANCHOR BLOCK 1255-PRA-VAL-IW-C-009
 - DETAIL R/F OF SURFACE INLET PLATFORM 1286-PRA-VAL-IW-C-008A
 - APPROACH BRIDGE RCC DETAILS OF FOUNDATION & SUBSTRUCTURE 1255-PRA-VAL-AB-C-001
 - LAYOUT PLAN & SECTIONAL ELEVATION OF PROPOSED SWITCH GEAR ROOM & SUBSTATION PLATFORM 1255-PRA-VAL-C-SWG-004.

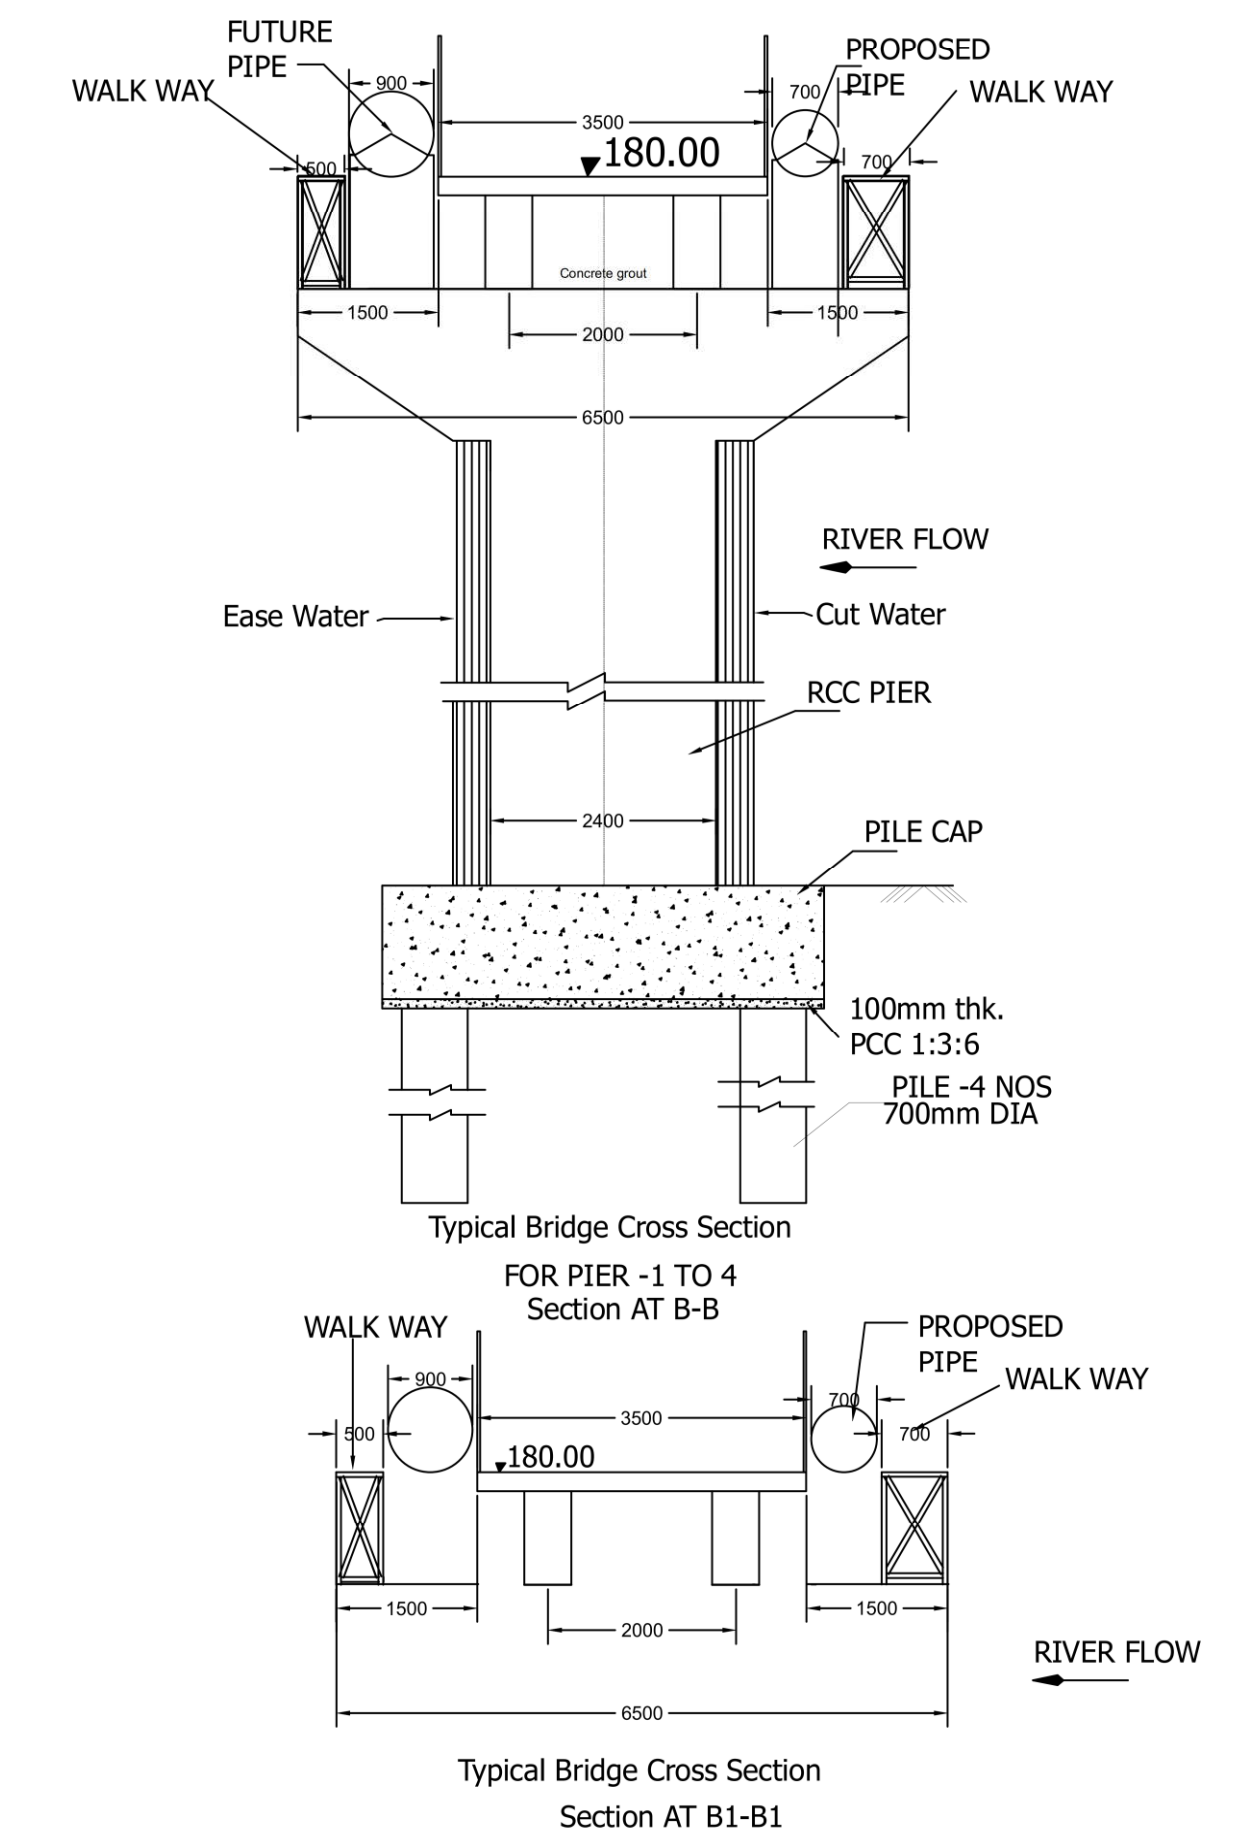

- TYPICAL DETAILS OF VEDANTA STANDARD**
- Note :**
- All levels are in meter and dimensions, bar Dia, spacing, weld thickness etc. are in mm UNLESS MENTIONED OTHERWISE.
 - No dimensions will be scaled off from the drawing.
 - This drawing supersede all previous drawings.
 - The Pile cap shall not be above the river Bed/Bank level in any case.

GOOD FOR CONSTRUCTION
DT. 23-05-2022 [R0]

Client :	VEDANTA LIMITED				
Project Consultant :	PRATHAMESH SOLUTIONS PROJECT ENGINEERING & MANAGEMENT CONSULTANTS OFF. : 29, 4 th Floor, Wing-C, "Shewalkar Gardens", Near IT Park, Opp. VIT, Coimbatore, Nagpur, India. Pin-461013 Email: prathameshconsultants@gmail.com, nrisagp@gmail.com, URL: http://www.prathamesh.co.in				
Project :	New Radial Intake Well at New location and Interconnection to Existing Pipeline				
Drawing Title :	New Radial Intake Well at New Location				
Drawing Sub Title :	GA OF INTAKE WELL, APPROACH BRIDGE				
Drawing No :	1286-PRA-VAL-C-DWG-002A				
Issued for :	EXECUTION				
Date	Drawn by :	Checked by :	Sheet Layout	Sheet No.:	Rev. No.:
23.05.2022	G.D.M.	N.S.J.	A1	1 of 1	00