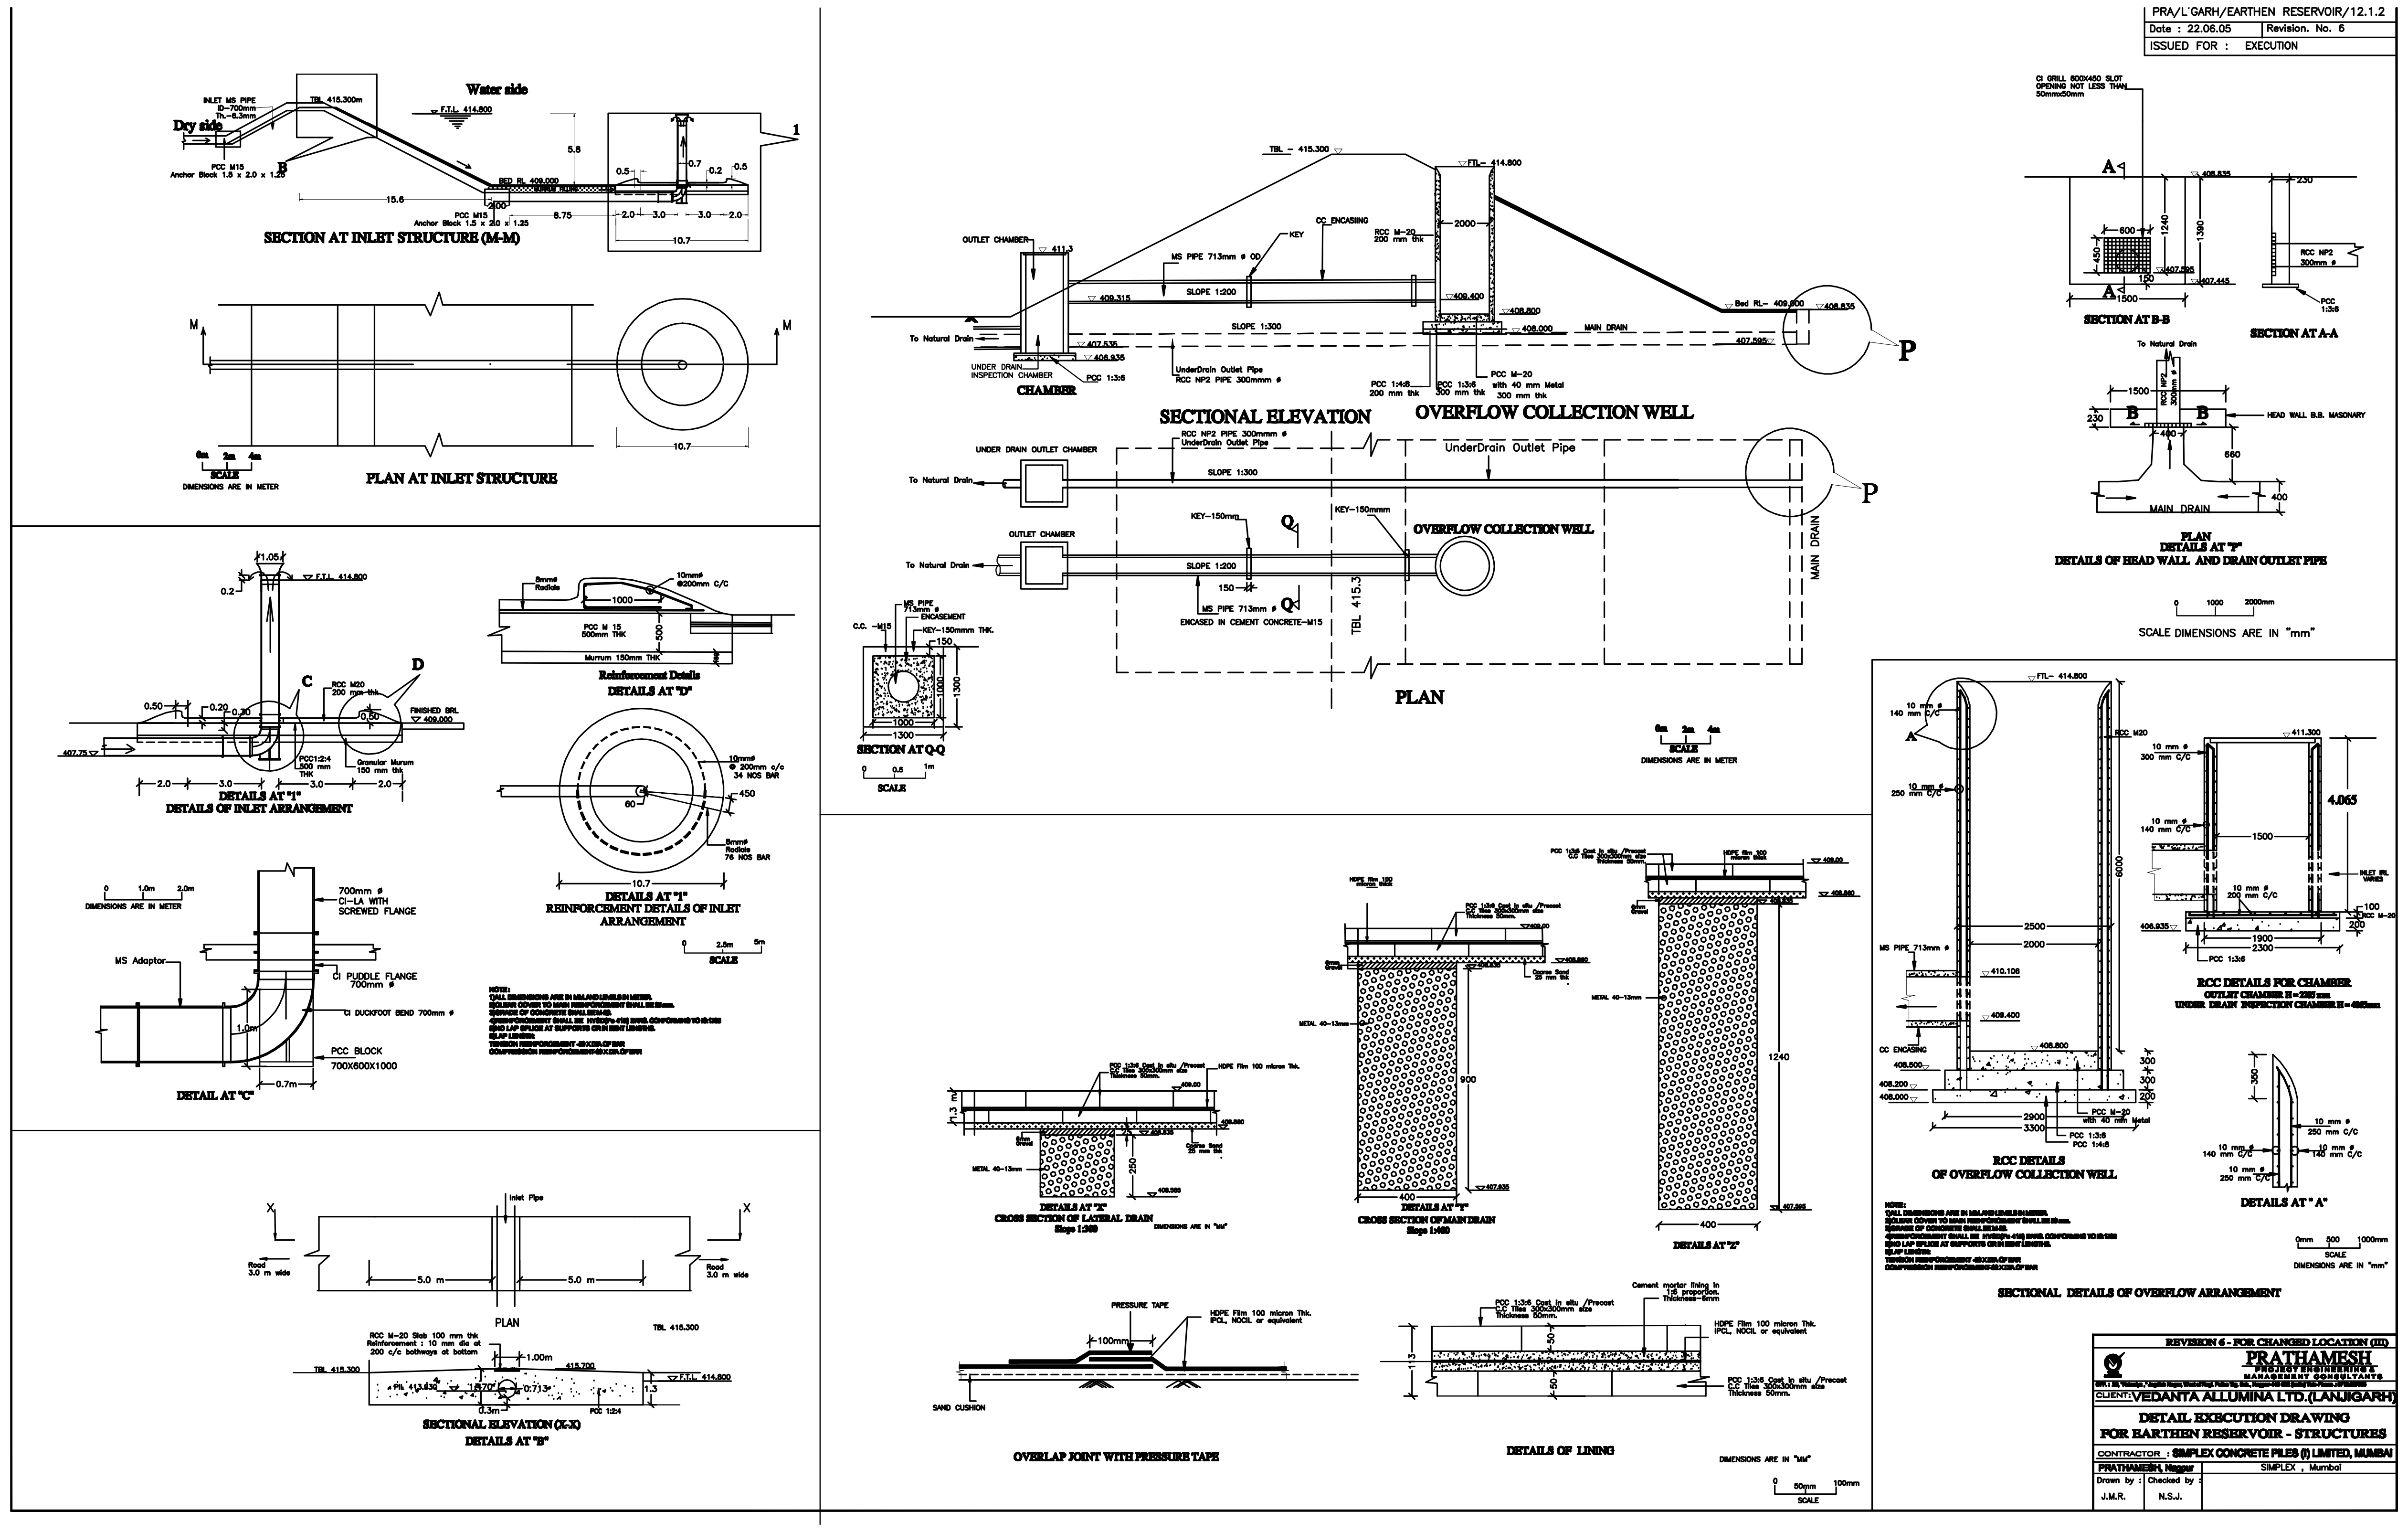
SECTION AT INLET STRUCTURE (M-M)
PLAN AT INLET STRUCTURE
Water side
Dry side
DETAILS AT "I"
DETAILS OF INLET ARRANGEMENT
DETAILS AT "D"
DETAILS AT "I"
REINFORCEMENT DETAILS OF INLET ARRANGEMENT
DETAIL AT "C"
SECTIONAL ELEVATION (X-X)
DETAILS AT "E"
SECTIONAL ELEVATION
OVERFLOW COLLECTION WELL
CHAMBER
PLAN
MAIN DRAIN
SECTION AT Q-Q
P
CROSS SECTION OF LATERAL DRAIN
CROSS SECTION OF MAIN DRAIN
DETAILS AT "Z"
OVERLAP JOINT WITH PRESSURE TAPE
DETAILS OF LINING
SECTION AT B-B
SECTION AT A-A
DETAILS OF HEAD WALL AND DRAIN OUTLET PIPE
SCALE DIMENSIONS ARE IN "mm"
RCC DETAILS OF OVERFLOW COLLECTION WELL
RCC DETAILS FOR CHAMBER
DETAILS AT " A"
0mm 500 1000mm
SCALE
DIMENSIONS ARE IN "mm"
SECTIONAL DETAILS OF OVERFLOW ARRANGEMENT

PRA/L'GARH/EARTHEN RESERVOIR/12.1.2
Date : 22.06.05 | Revision. No. 6
ISSUED FOR : EXECUTION

REVISION 6 - FOR CHANGED LOCATION (III)
PRATHAMESH
PROJECT ENGINEERING & MANAGEMENT CONSULTANTS
CLIENT: VEDANTA ALLUMINA LTD.(LANJIGARH)
DETAIL EXECUTION DRAWING
FOR EARTHEN RESERVOIR - STRUCTURES
CONTRACTOR : SIMPLEX CONCRETE PILES (I) LIMITED, MUMBAI
PRATHAMESH, Nagpur | SIMPLEX , Mumbai
Drawn by : J.M.R. | Checked by : N.S.J.

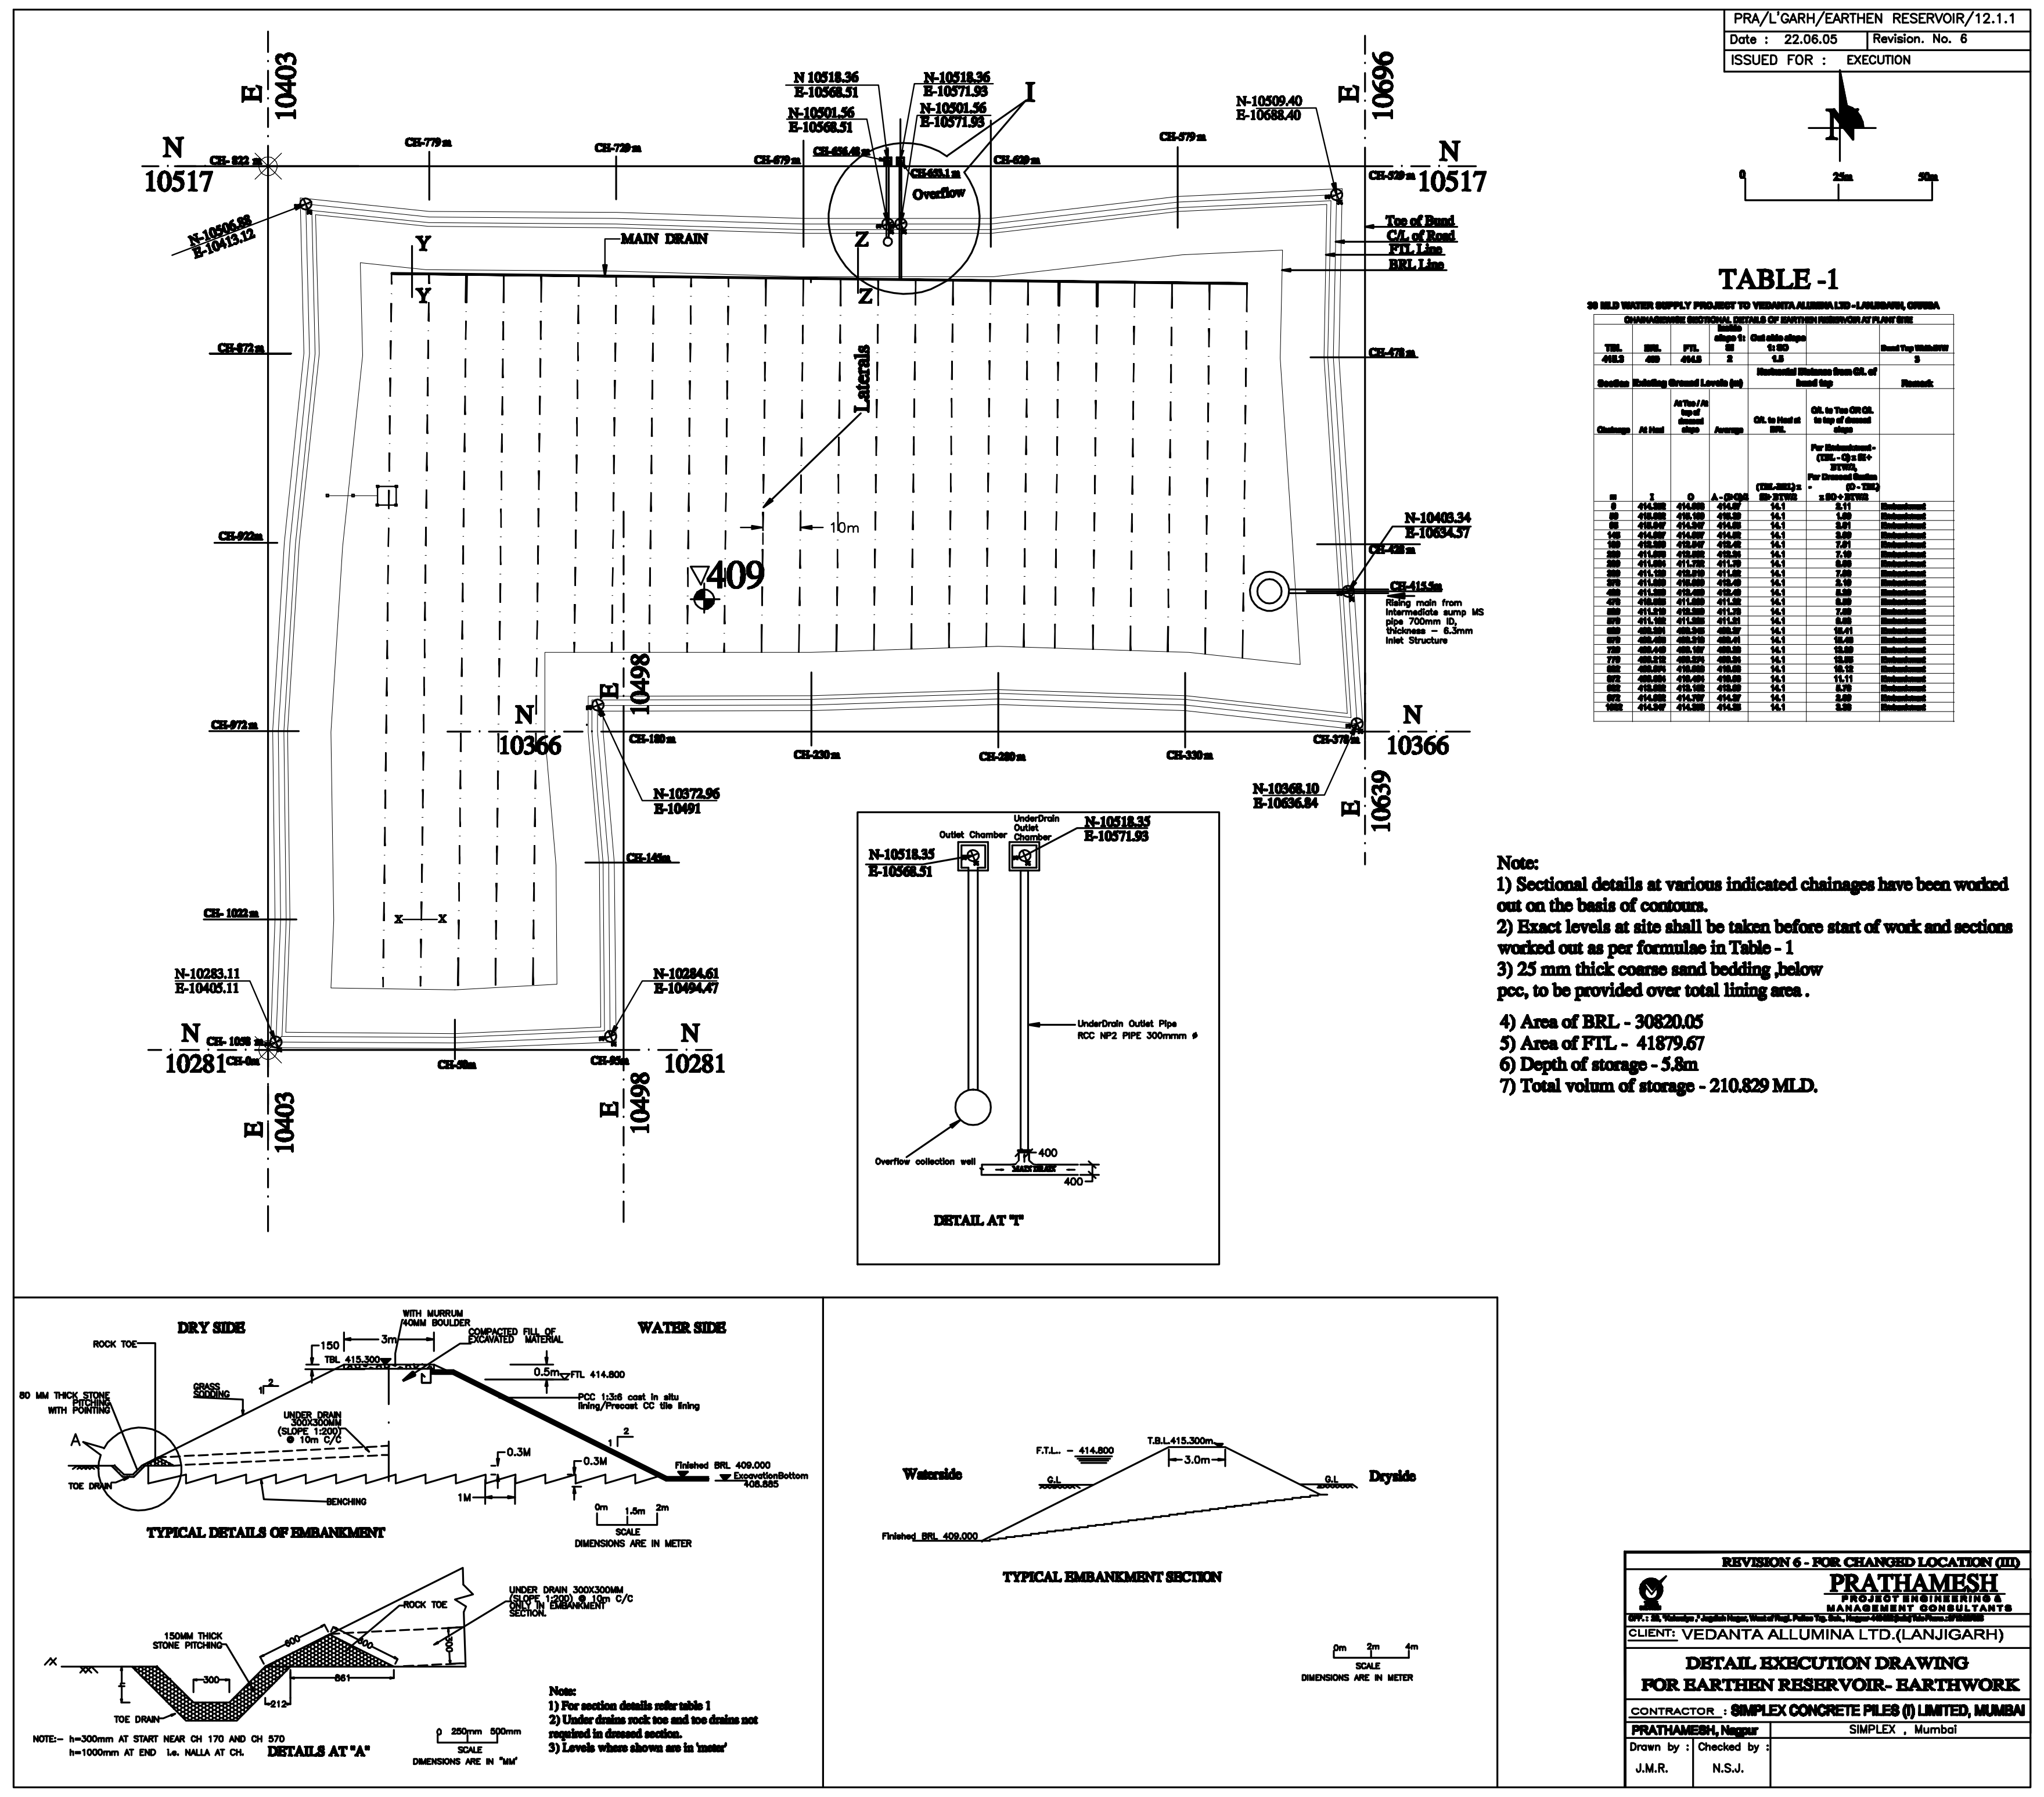

PRA/L'GARH/EARTHEN RESERVOIR/12.1.1
Date : 22.06.05 | Revision. No. 6
ISSUED FOR : EXECUTION

TABLE -1

Note:
1) Sectional details at various indicated chainages have been worked out on the basis of contours.
2) Exact levels at site shall be taken before start of work and sections worked out as per formulae in Table - 1
3) 25 mm thick coarse sand bedding ,below pcc, to be provided over total lining area .
4) Area of BRL - 30820.05
5) Area of FTL - 41879.67
6) Depth of storage - 5.8m
7) Total volum of storage - 210.829 MLD.

REVISION 6 - FOR CHANGED LOCATION (III)
PRATHAMESH
PROJECT ENGINEERING & MANAGEMENT CONSULTANTS
CLIENT: VEDANTA ALLUMINA LTD.(LANJIGARH)
DETAIL EXECUTION DRAWING
FOR EARTHEN RESERVOIR- EARTHWORK
CONTRACTOR : SIMPLEX CONCRETE PILES (I) LIMITED, MUMBAI
PRATHAMESH, Nagpur | SIMPLEX , Mumbai
Drawn by : J.M.R. | Checked by : N.S.J.

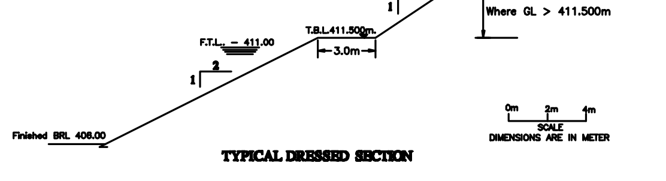

TYPICAL DRESSED SECTION